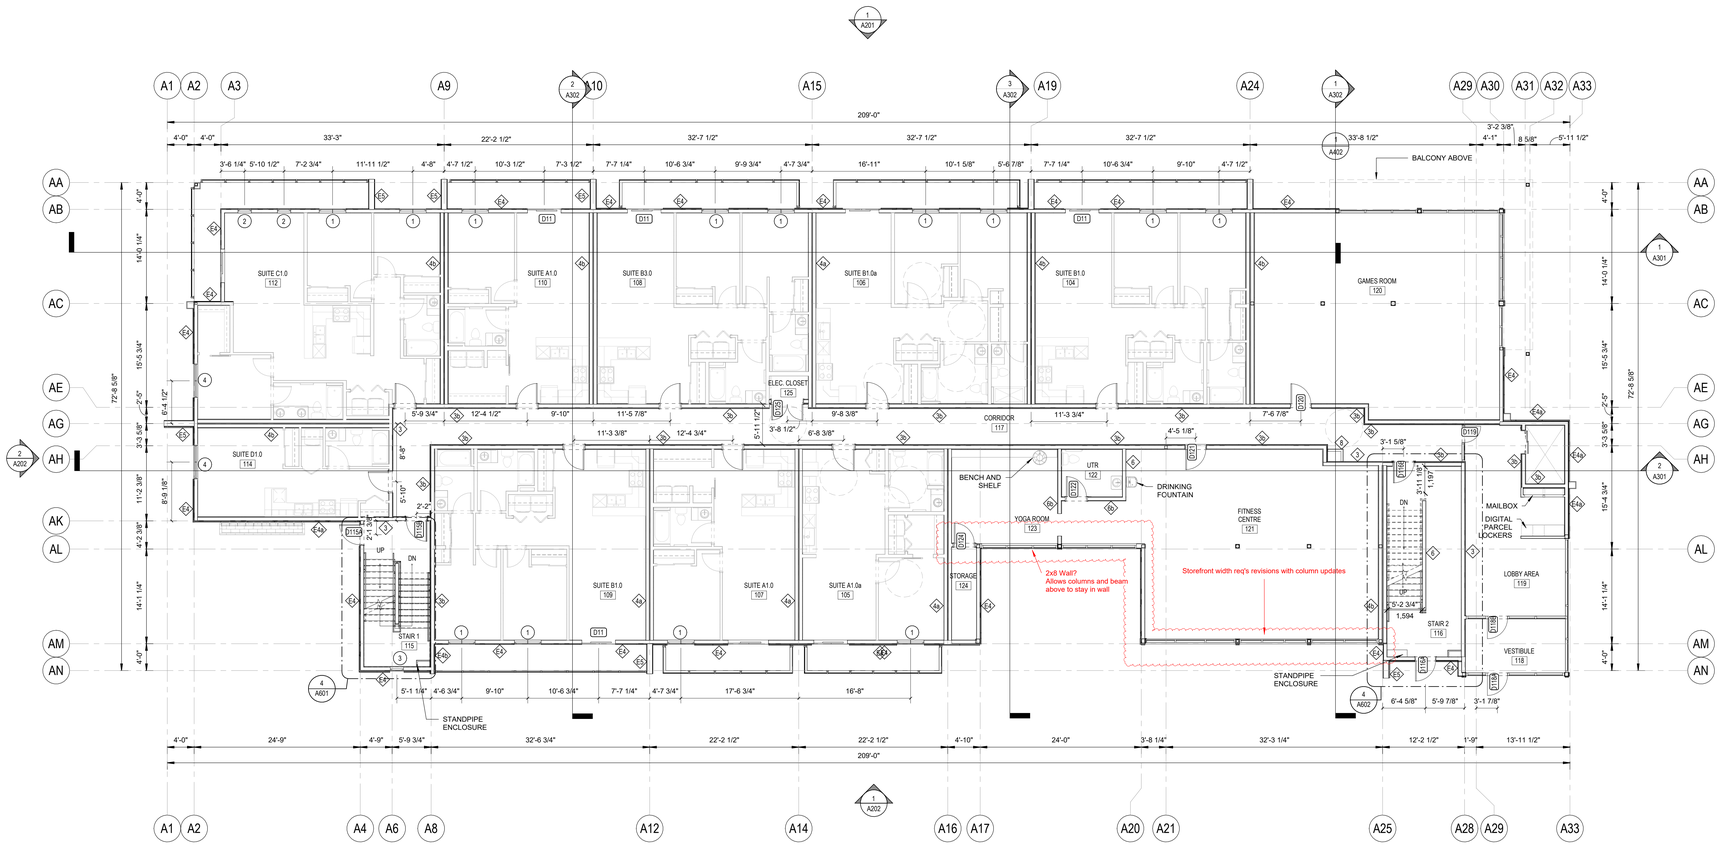

1 A111 BUILDING A - MAIN FLOOR PLAN
1/8" = 1'-0"

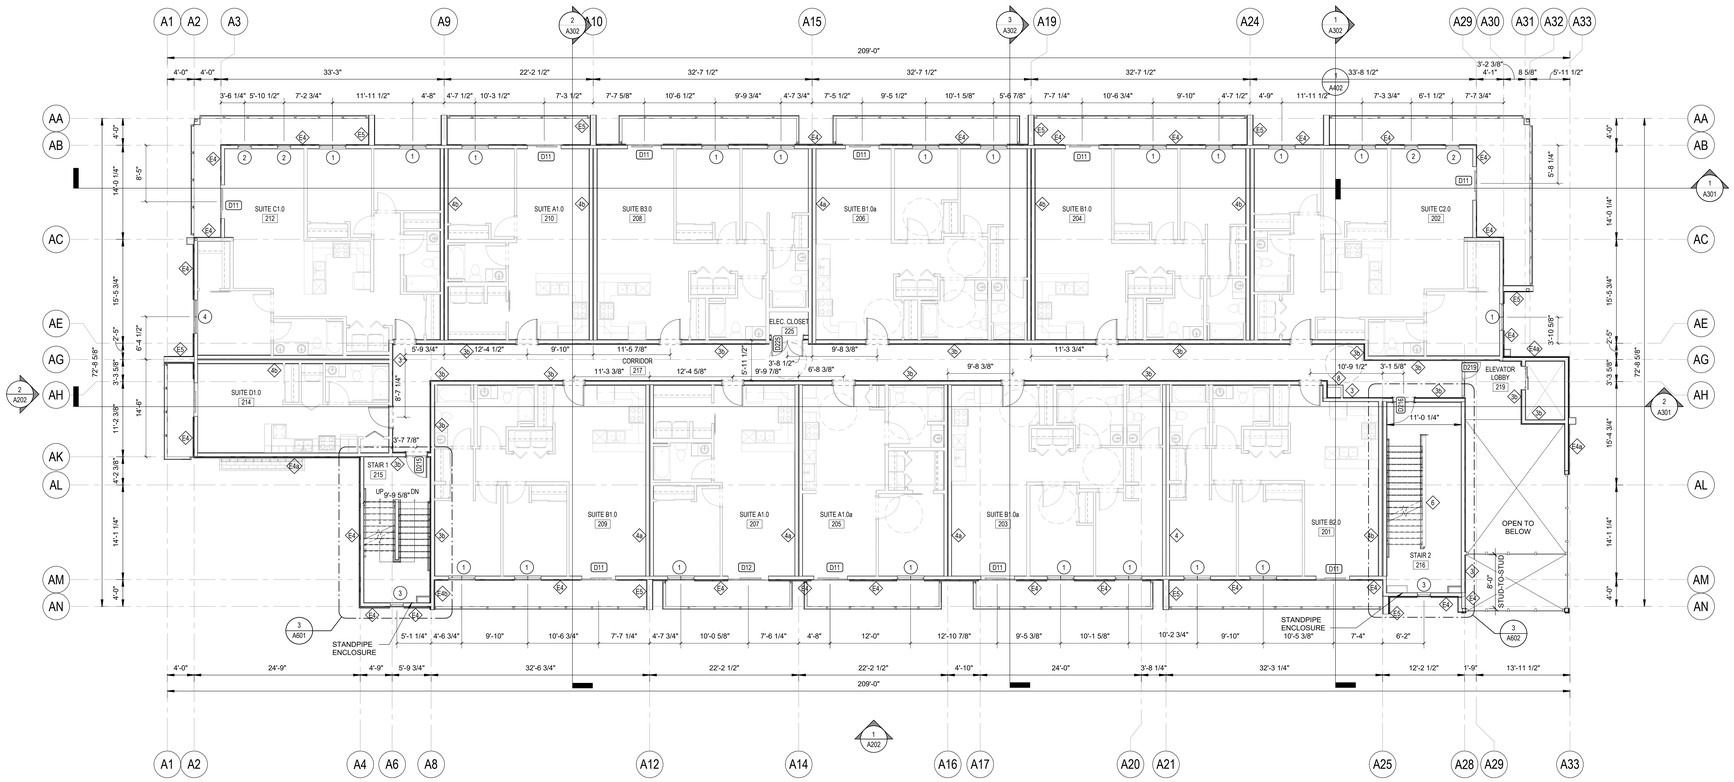

2 A111 BUILDING A - SECOND FLOOR PLAN
1/8" = 1'-0"

Ironclad Developments Inc.
IRONCLAD DEVELOPMENTS INC.
www.ironcladdevelopments.ca
Project Management
General Contracting
Design/ Build
101- 57158 Symington Road,
Springfield, MB
R2J 4L6
Ph: 204-777-1972
info@iodev.ca

REV#	Revision Description	Date
0	ISSUED FOR BUILDING PERMIT	OCT 17, 2025

Consultant
ARCHITECTURE INC
201 -57158 Symington Rd 20E.
Springfield, MB R2J 4L6
T:2042279274
E: RGARVEY@A77.CA

All drawings and specifications are the property of Ironclad Developments Inc. and cannot be reproduced or used without written consent. The contractor shall verify all dimensions, datums and levels noted on the drawings with the conditions on site and shall be responsible for reporting any errors or omissions to the Architect for adjustments. This drawing shall not be scaled.

Seal

Project
HARBOUR HILLS

325 WATFIELD AVENUE
NANAIMO, BC

Drawing Title
BLDG A - MAIN AND SECOND FLOOR PLAN

Project no.	A600	Designed by	RG
Drawn by	MC	Reviewed by	RG
Date	OCTOBER 17, 2025	Scale	1/8" = 1'-0"
Sheet no.	A111	Revision no.	0

KEY PLAN

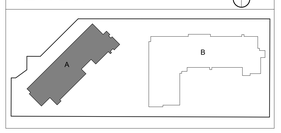

2025-10-17-4:34:56 PM Autodesk Docs://Harbour Hills/2104_HBH_Arch Project File.rvt