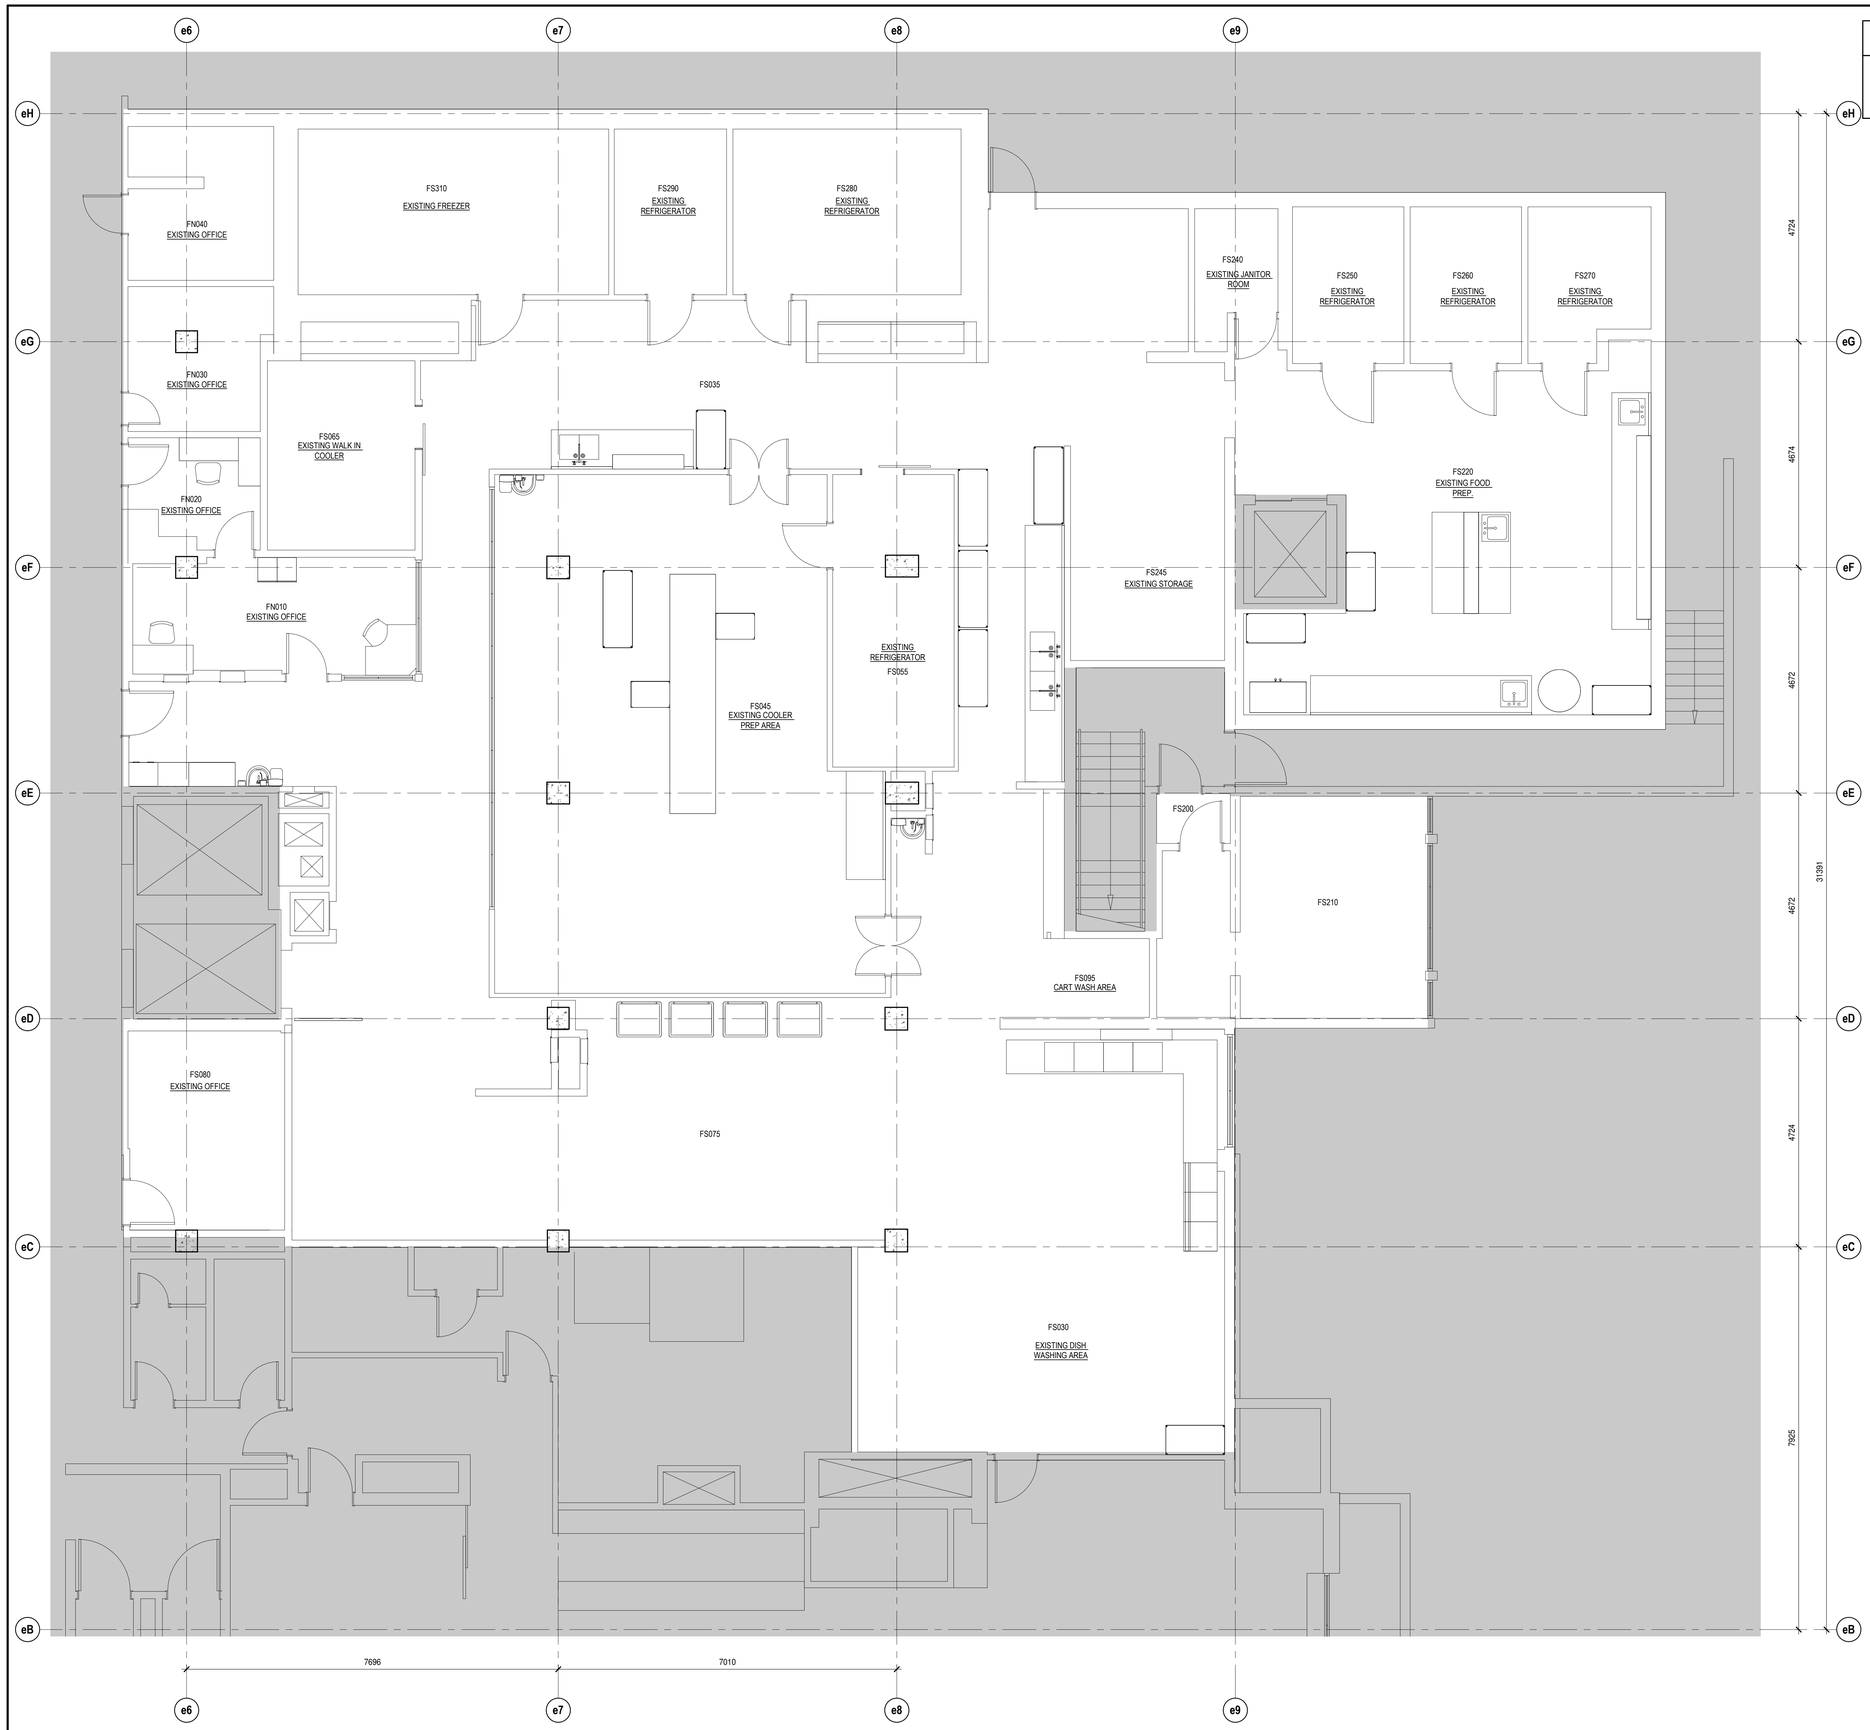

1 A-100 LEVEL 1 - OVERALL EXISTING PLAN
SCALE: 1 : 50

GRAPHICS LEGEND

AREA OUTSIDE CURRENT PHASE

fraserhealth
Better health. Best in health care.

kasian

Kasian Architecture
Interior Design
and Planning Ltd

1500 West Georgia Street, Suite 1685
Vancouver, BC Canada V6G 2Z6
T 604 683 4145 F 604 683 2927
www.kasian.com

N

REV.	YYYY-MM-DD	REVISION / DRAWING ISSUE	REVIEW
5	2025.03.21	ISSUE FOR 95% CD REVIEW	
4	2025.03.07	ISSUE FOR BUILDING PERMIT	
3	2025.02.21	ISSUE FOR 50% CD REVIEW	
2	2024.01.20	ISSUE FOR DD REVIEW	
1	2024.12.20	ISSUE FOR DRAFT DD REVIEW	

CONSULTANT

PERMIT STAMP

SEAL

THIS DRAWING, AS AN INSTRUMENT OF SERVICE, IS THE PROPERTY OF KASIAN ARCHITECTURE INTERIOR DESIGN AND PLANNING LTD. THE COPYRIGHT IN THE SAME BEING RESERVED TO THEM. NO REPRODUCTION IS ALLOWED WITHOUT THE PERMISSION OF KASIAN ARCHITECTURE INTERIOR DESIGN AND PLANNING LTD AND WHEN MADE MUST BEAR ITS NAME.
THIS DRAWING IS NOT TO BE SCALED. THE CONTRACTOR IS TO VERIFY DIMENSIONS AND DATA NOTED HEREIN WITH THE CONDITIONS ON SITE AND IS RESPONSIBLE FOR REPORTING ANY DISCREPANCY TO KASIAN ARCHITECTURE INTERIOR DESIGN AND PLANNING LTD FOR ADJUSTMENT.

PROJECT

PEACH ARCH HOSPITAL New Production Kitchen

15521 Russell Ave.
White Rock, BC, Canada

DRAWING TITLE

LEVEL 1 - OVERALL EXISTING PLAN

DRAWING ISSUE

ISSUE FOR 95% CD REVIEW

PROJECT NO.	PLOT DATE	DRAWN
270014	2024-10-25	Author
	SCALE: 1 : 50	REVIEWED: Checker

DRAWING NO. A-100

REVISION 5